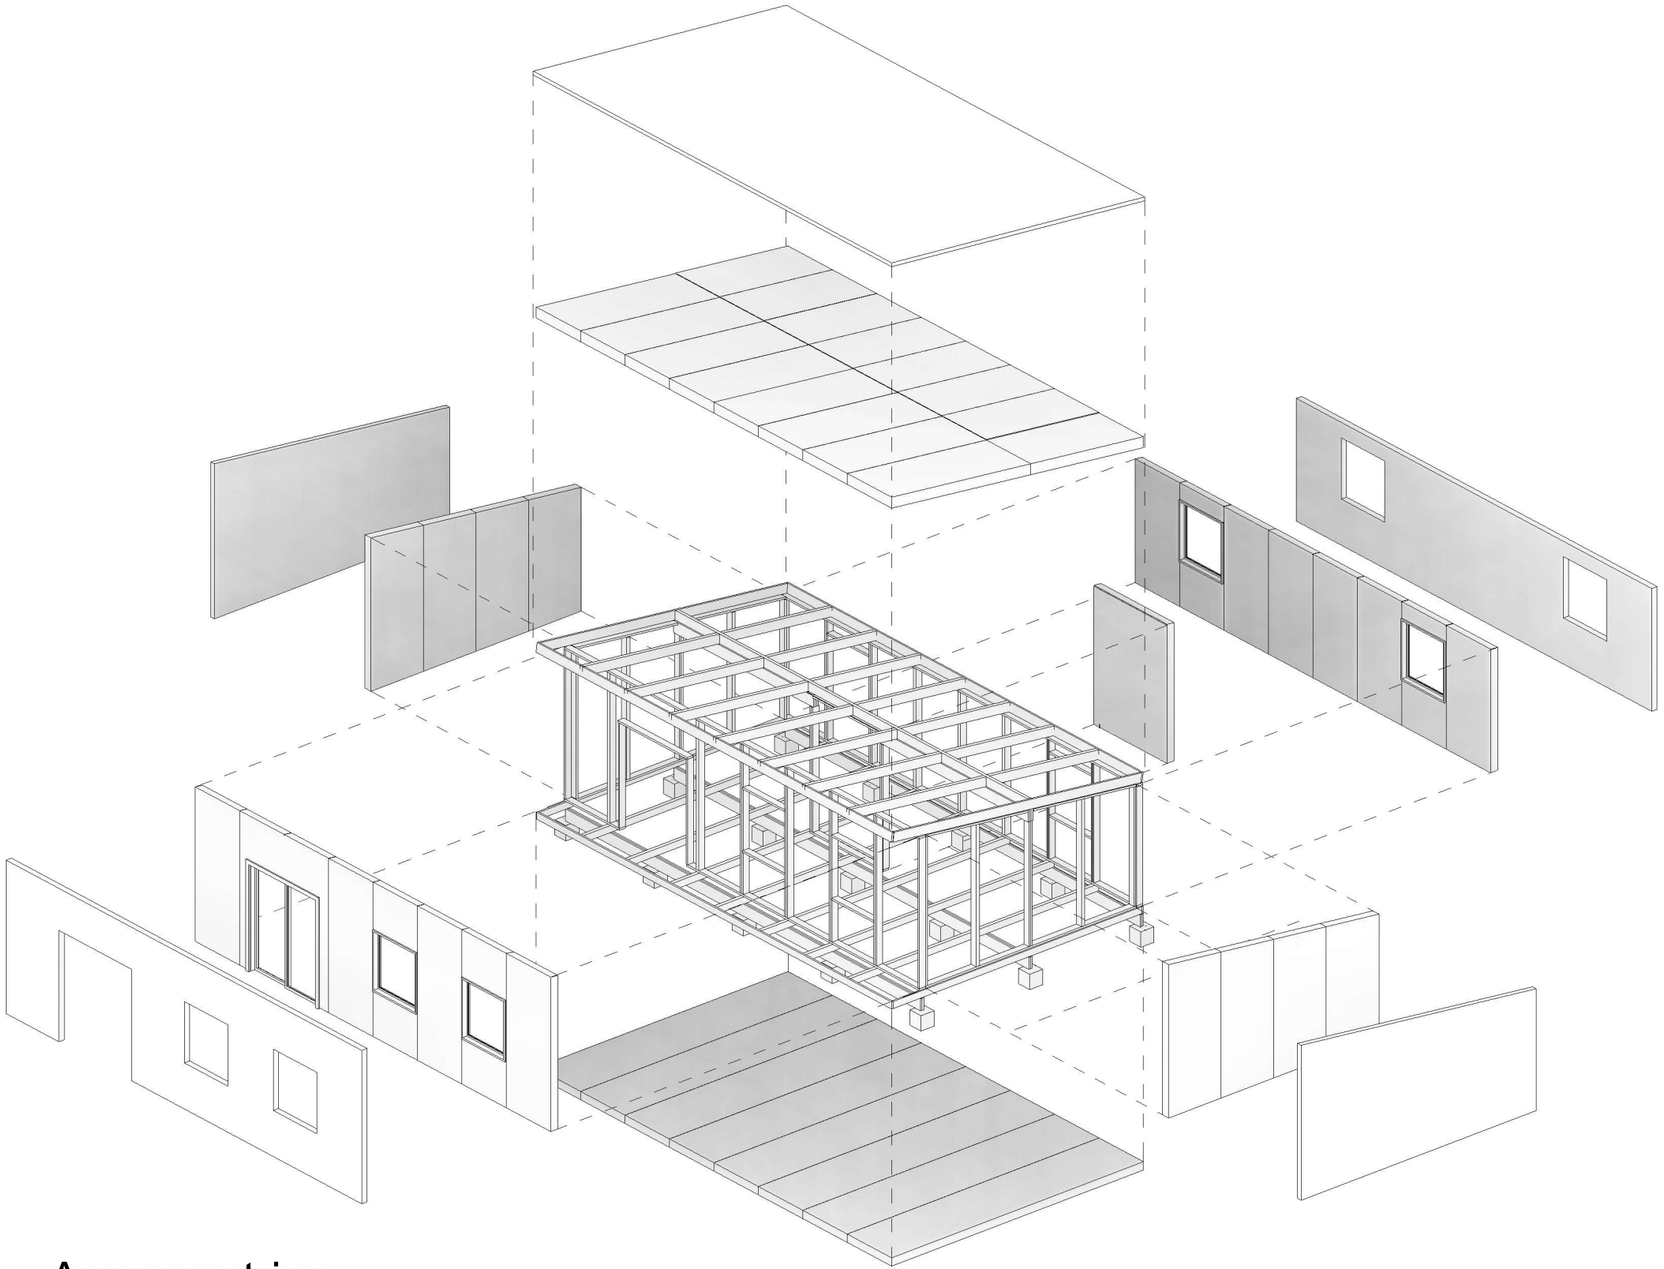

1 Axonometrico

PREFLEX

ADU 16X32

PREFLEX HOMES

No.	Description	Date

ADU 16X32 3D View

Project number	P017.3
Date	FEB/15/2022
Drawn by	OD
Checked by	Checker

A100

Scale

03/05/2022 03:58:23 p. m.

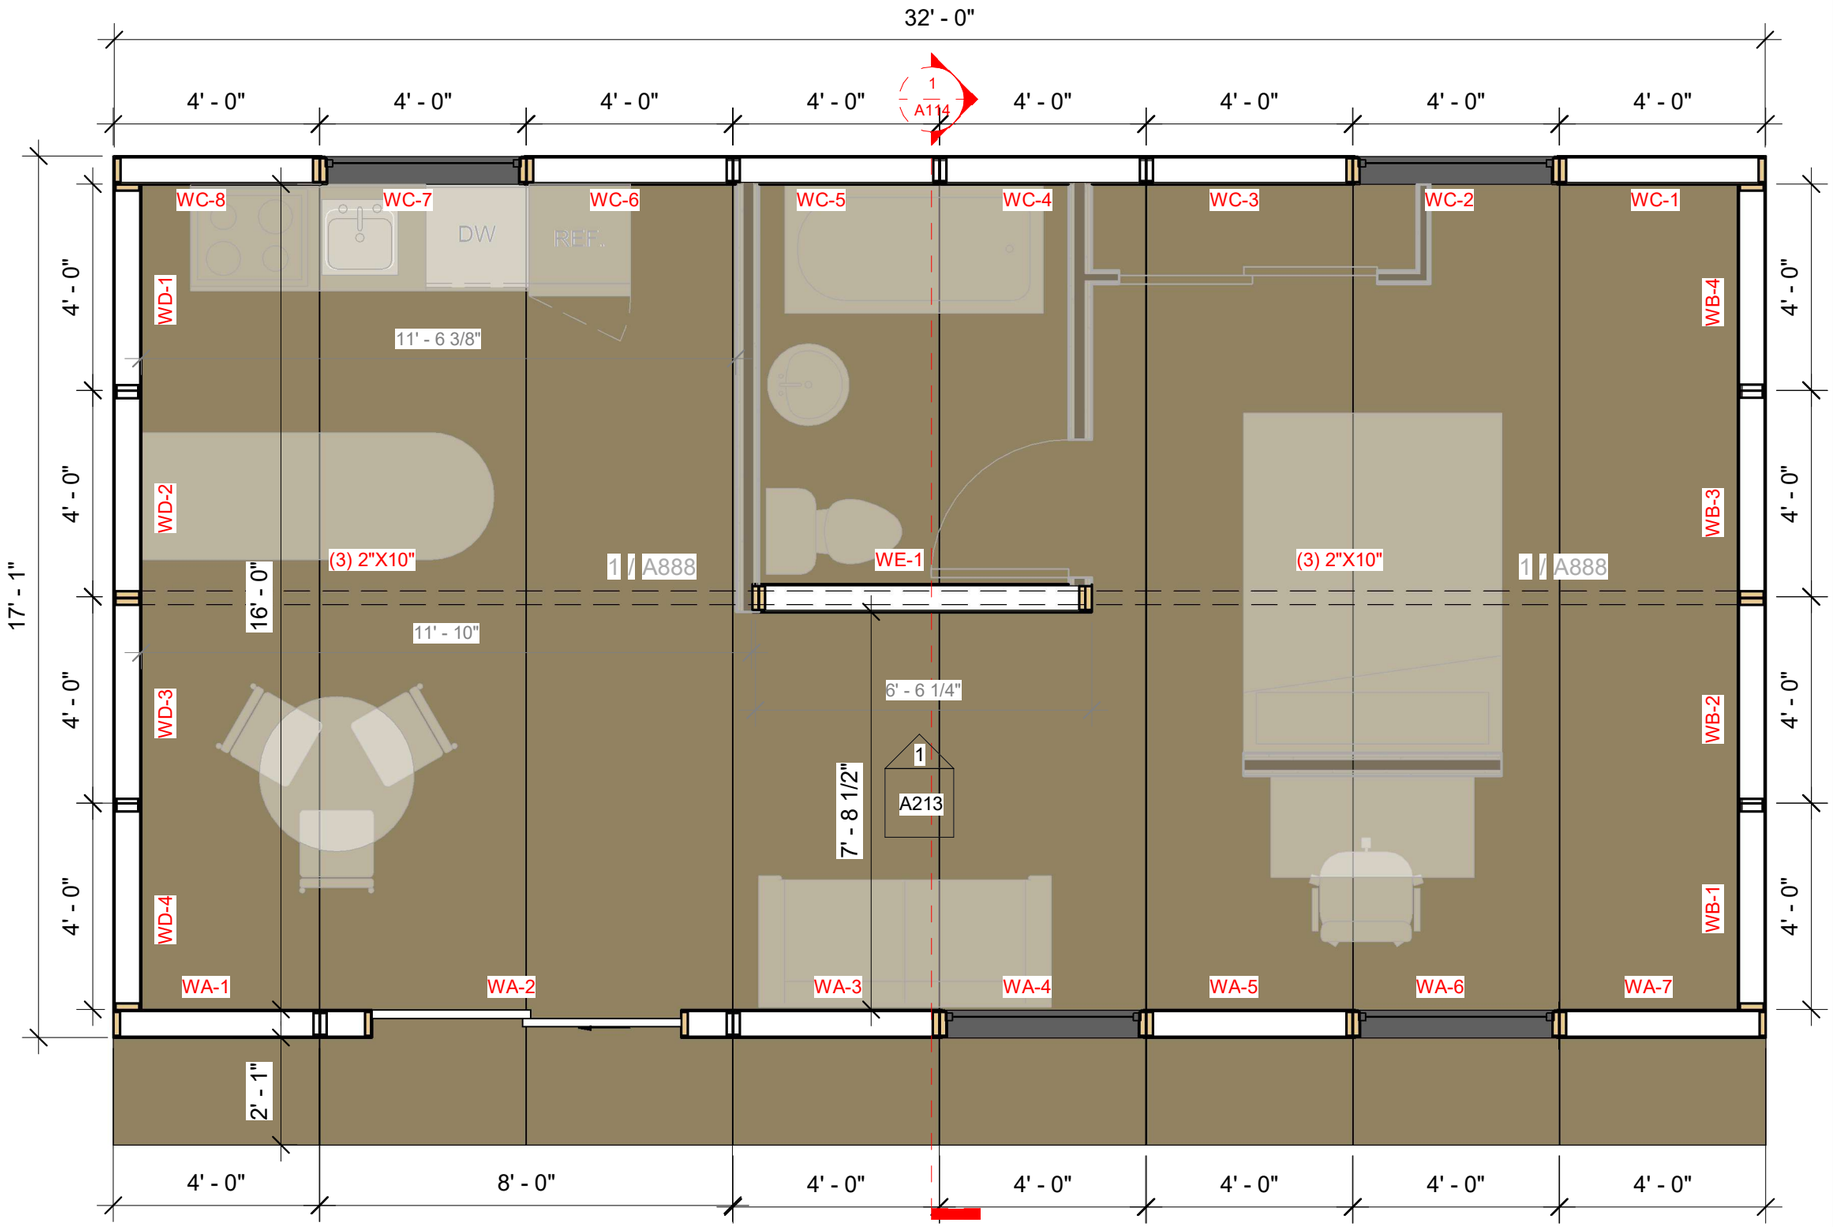

1 Floor Plan

3/8" = 1'-0"

PREFLEX

ADU 16X32

PREFLEX HOMES

No.	Description	Date

ADU 16X32

Project number	P017.3
Date	FEB/15/2022
Drawn by	JV
Checked by	GG
A101	
Scale	3/8" = 1'-0"

03/05/2022 03:58:24 p. m.

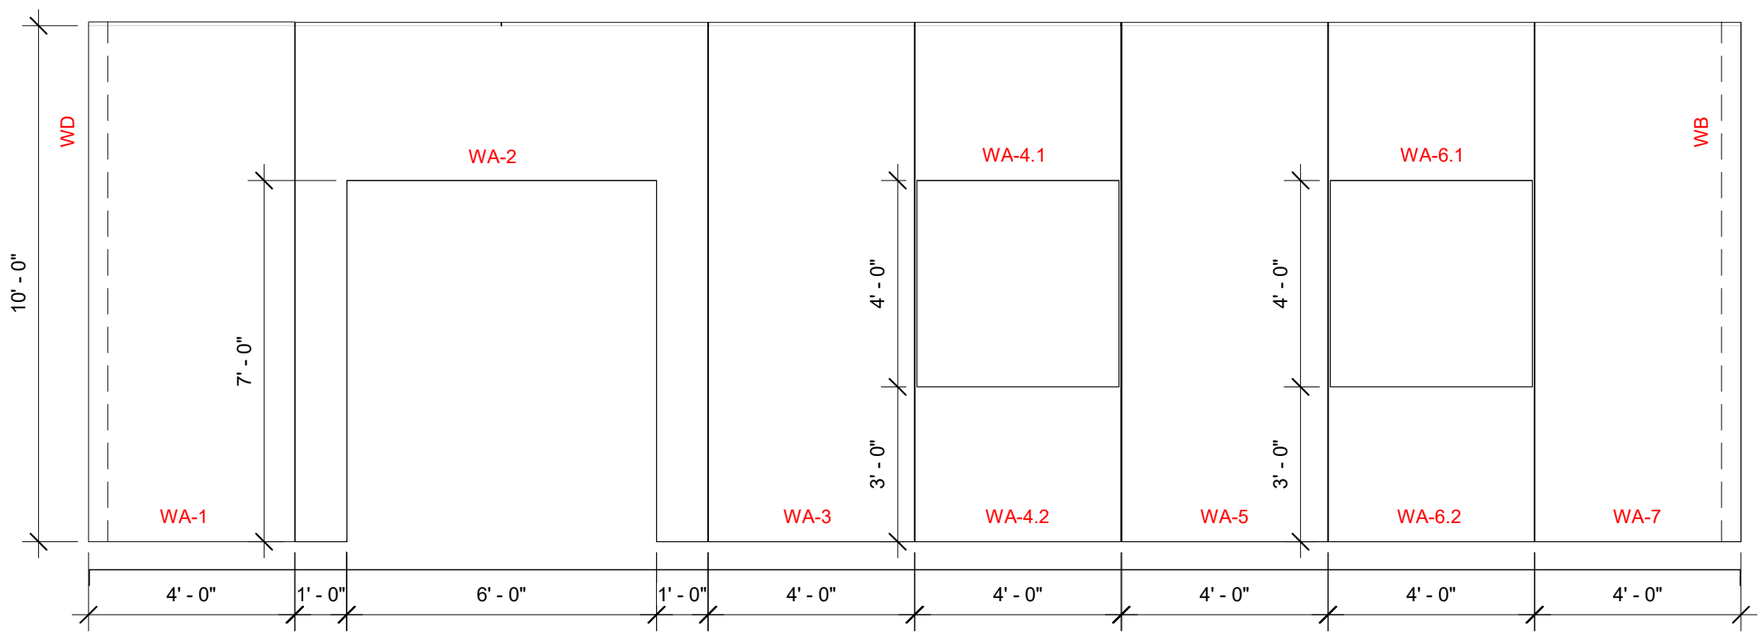

2 WA Wall
3/8" = 1'-0"

PREFLEX

ADU 16X32

PREFLEX HOMES

No.	Description	Date

Elevations

Project number	P017.3
Date	FEB/15/2022
Drawn by	JV
Checked by	FT

A103

Scale 3/8" = 1'-0"

03/05/2022 03:58:24 p. m.

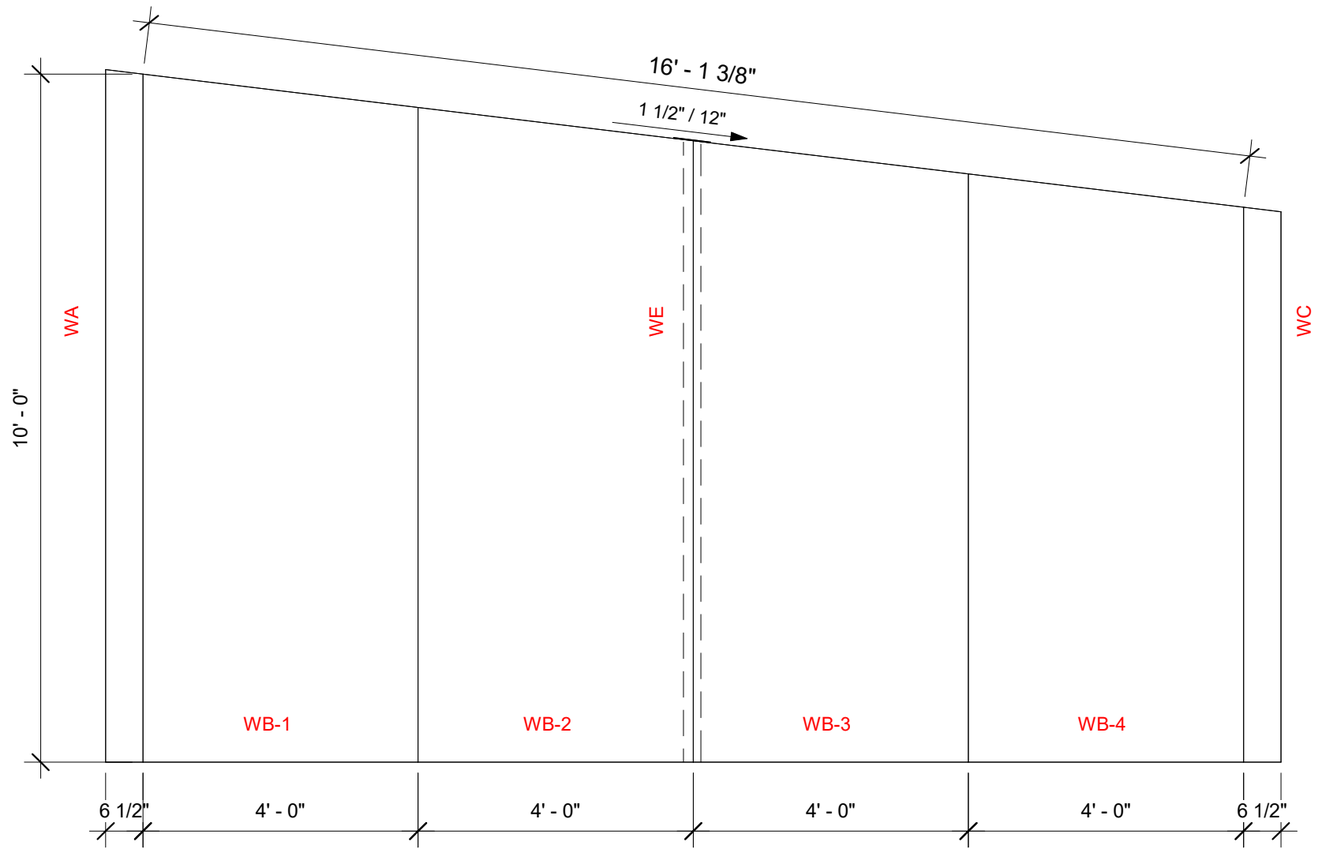

1 WB Wall
1/2" = 1'-0"

PREFLEX

ADU 16X32

PREFLEX HOMES

No.	Description	Date

Elevations

Project number	P017.3
Date	FEB/15/2022
Drawn by	OD
Checked by	Checker
	A104
Scale	1/2" = 1'-0"

03/05/2022 03:58:24 p. m.

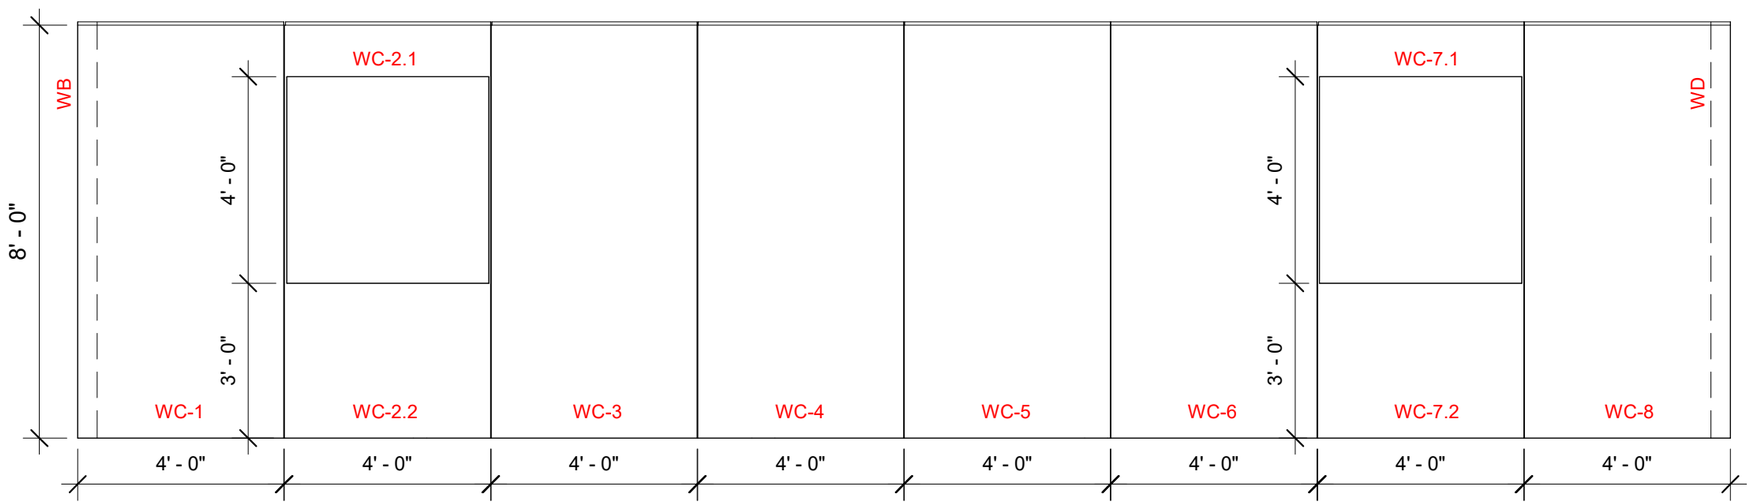

1 WC Wall

3/8" = 1'-0"

PREFLEX

ADU 16X32

PREFLEX HOMES

No.	Description	Date

Elevations

Project number	P017.3
Date	FEB/15/2022
Drawn by	OD
Checked by	Checker
A105	
Scale	3/8" = 1'-0"

03/05/2022 03:58:25 p. m.

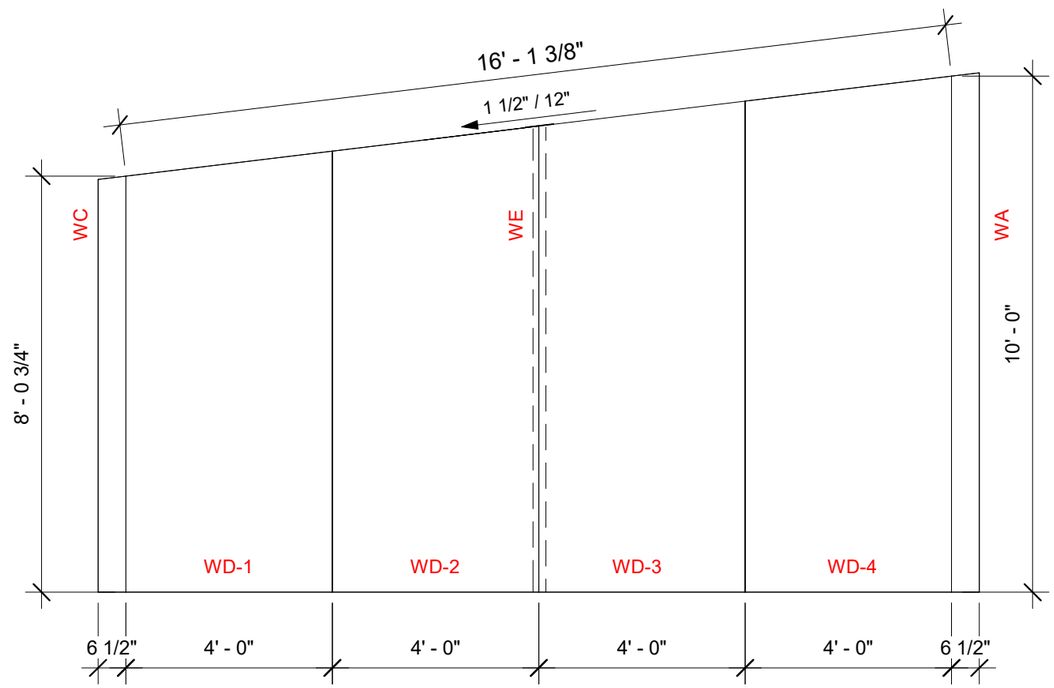

1 WD Wall

3/8" = 1'-0"

PREFLEX

ADU 16X32

PREFLEX HOMES

No.	Description	Date

Elevations

Project number	P017.3
Date	FEB/15/2022
Drawn by	OD
Checked by	Checker

A106

Scale 3/8" = 1'-0"

03/05/2022 03:58:25 p. m.

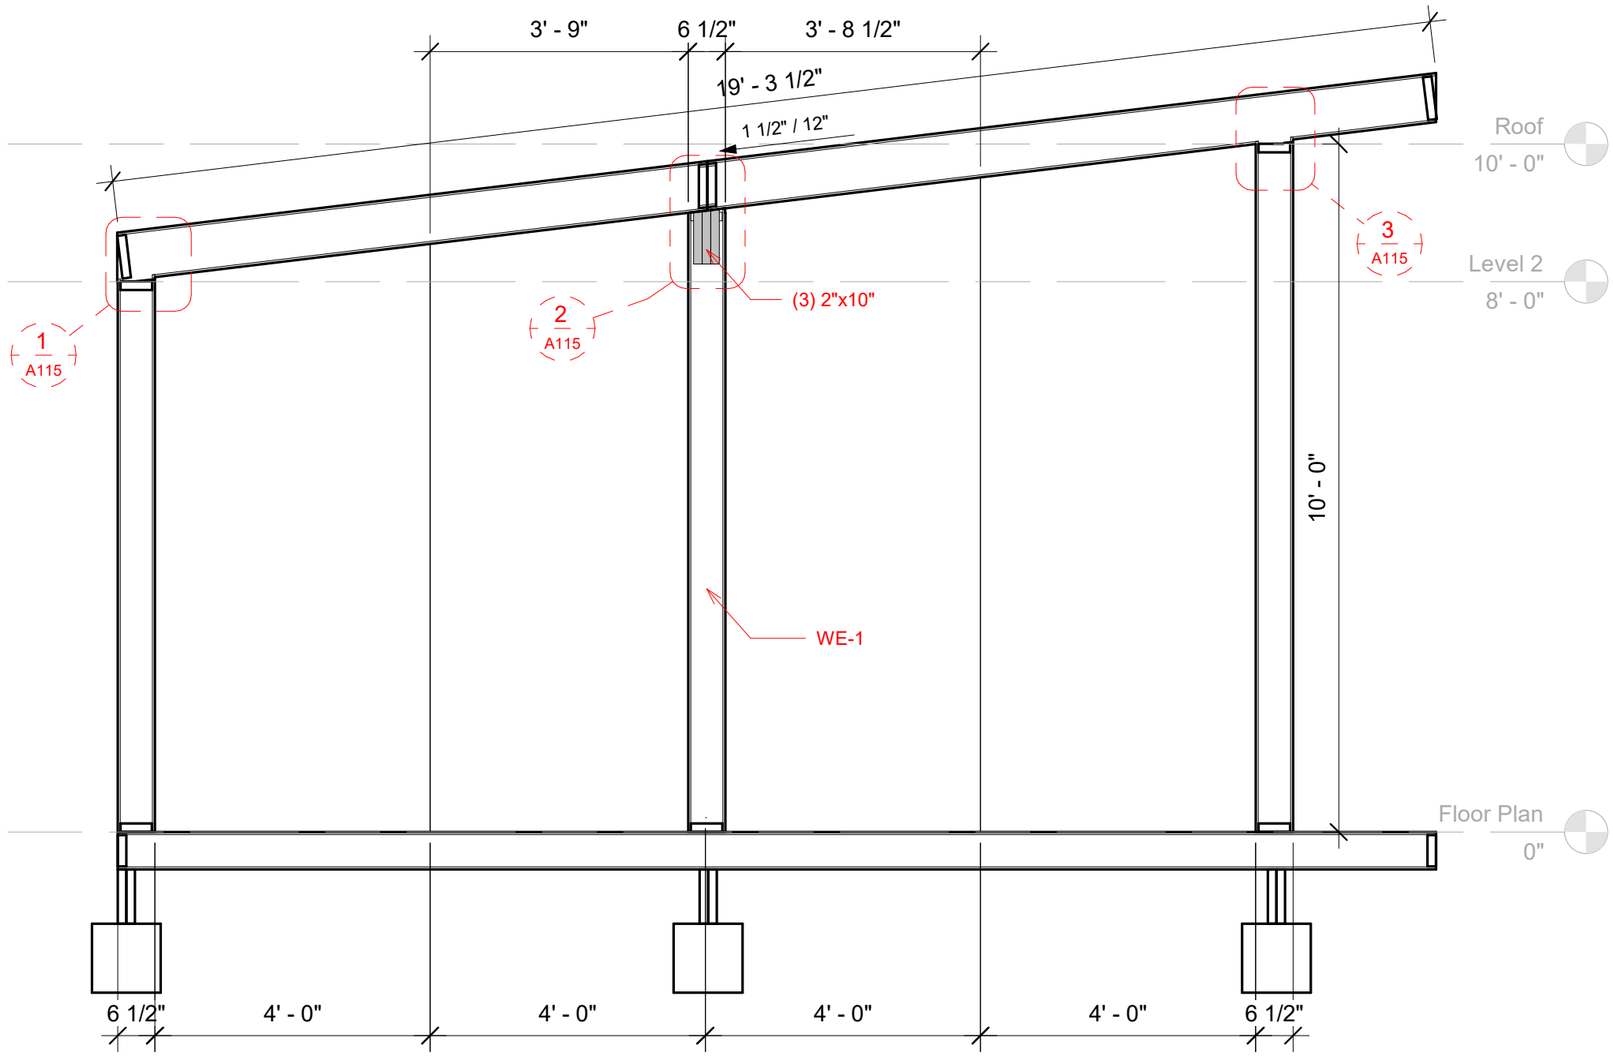

1 Section
1/2" = 1'-0"

PREFLEX

ADU 16X32

PREFLEX HOMES

No.	Description	Date

Section

Project number	P017.3
Date	FEB/15/2022
Drawn by	JV
Checked by	FT

A114

Scale 1/2" = 1'-0"

03/05/2022 03:58:25 p. m.